



การไฟฟ้าส่วนภูมิภาค PROVINCIAL ELECTRICITY AUTHORITY

จาก ผบส.กฟส.หาดใหญ่ ถึง กฟส.หาดใหญ่
เลขที่ วันที่
เรื่อง ขออนุมัติขยายเขตระบบจำหน่ายไฟฟ้าให้กับ แขนงทางหลวงสงขลาที่ ๑ หน้าศูนย์กระจายสินค้า (จุดที่ ๒) บริเวณ ทางหลวงหมายเลข ๔ ตอนควบคุม ๑๔๐๑ ตอนพรุพ้อ-เนินพิชัย ระหว่าง กม. ๑๒๔๔+๒๕๐-กม.๑๒๔๕+๑๐๐ ตำบลท่าช้าง อำเภอบางกล่ำ จังหวัดสงขลา
อ้างถึง อ้างถึงคำร้องขยายเขตฯ เลขที่ LHAY๖๙๐๐๒๕๐๗ ลว. ๑๔ ก.ค. ๖๙
สิ่งที่ส่งมาด้วย ๑. แผนผังแบบเลขที่ TFO๙-๐Am/๖๙๐๗๙๖ จำนวน ๑ แผ่น
๒.ประมาณการ จำนวน ๑ ชุด

เรียน ผจก.กฟส.หาดใหญ่

ตามคำร้องขยายเขตระบบจำหน่ายไฟฟ้า เลขที่ LHAY๖๙๐๐๒๕๐๗ ลว. ๑๔ ก.ค. ๖๙ ให้กับ แขนงทางหลวงสงขลาที่ ๑ กรมทางหลวง หน้าศูนย์กระจายสินค้า (จุดที่ ๒) บริเวณ ทางหลวงหมายเลข ๔ ตอนควบคุม ๑๔๐๑ ตอนพรุพ้อ-เนินพิชัย ระหว่าง กม.๑๒๔๔+๒๕๐-กม.๑๒๔๕+๑๐๐ ตำบลท่าช้าง อำเภอบางกล่ำ จังหวัดสงขลา นั้น

ผบส.กฟส.หาดใหญ่ ได้ตรวจสอบและพิจารณาแล้วสรุปได้ ดังนี้

๑. รายละเอียด

๑.๑ สถานที่ขอใช้ไฟเป็น แขนงทางหลวงสงขลาที่ ๑ กรมทางหลวง บริเวณ หน้าศูนย์กระจายสินค้า (จุดที่ ๒) ทางหลวงหมายเลข ๔ ตอนควบคุม ๑๔๐๑ ตอนพรุพ้อ-เนินพิชัย ระหว่าง กม.๑๒๔๔+๒๕๐-กม. ๑๒๔๕+๑๐๐ ตำบลท่าช้าง อำเภอบางกล่ำ จังหวัดสงขลา

๑.๒ ลูกคามีความประสงค์ขยายเขต ติดตั้งหม้อแปลงขนาด ๓๐ เควีเอ ระบบ ๑ เฟส ๑๙,๐๐๐-๔๘๐/๒๔๐ โวลต์ จำนวน ๑ เครื่อง (แบบแขวน) โดยให้การไฟฟ้าส่วนภูมิภาคเป็นผู้ดำเนินการให้ทั้งหมด

๑.๓ ระบบจำหน่ายแรงสูงของการไฟฟ้าส่วนภูมิภาครับไฟจากสถานีจ่ายไฟ RTP๑๐ อยู่ห่างจากสถานีประมาณ ๑๓ กม.

๑.๔ สภาพพื้นที่หน้างาน การคมนาคมขนส่งไม่สะดวก เห็นควรคิดค่าแรงกรณี ๓

๓. วิธีดำเนินการ

กฟภ.ดำเนินการเอง

๓.๑ แผนหม้อแปลงภายใน ติดตั้งหม้อแปลง ขนาด ๓๐ เควีเอ ระบบ ๑ เฟส ๑๙,๐๐๐-๔๘๐/๒๔๐ โวลต์ จำนวน ๑ เครื่อง พร้อมอุปกรณ์ ป้องกันสัตว์ TR ๒๐๒ ครบชุด (แบบแขวน)

๓.๒. แผนมิเตอร์ ติดตั้งมิเตอร์แรงต่ำ ขนาด ๕(๑๐๐) แอมป์ ระบบ ๑ เฟส จำนวน ๑ ชุด

๔. ค่าใช้จ่าย

๔.๑. ค่าใช้จ่ายที่ คิดจากผู้ใช้ไฟ

แผนหม้อแปลงภายใน	๑๕๐,๔๖๗.๘๓	บาท
อุปกรณ์จับยึดหม้อแปลงป้องกันการโจรกรรม (Nut lock)	๓,๐๐๐.๐๐	บาท
แผนหม้อแปลงภายใน(ชุดกราวด์แรงต่ำทองแดง)	๕,๗๐๘.๒๕	บาท
ค่าสมทบแรงสูง (๓๐ คิวเอ็กซ์๑๐๐)	๓,๐๐๐.๐๐	บาท
ค่าเชื่อมแรงสูง	๑๔,๐๐๐.๐๐	บาท

การไฟฟ้าส่วนภูมิภาค

กำไรขั้นต้น	๓๑,๘๓๕.๒๒	บาท
รวม	๒๐๘,๐๑๑.๓๐	บาท
ภาษีมูลค่าเพิ่ม ๗ %	๑๔,๕๖๐.๗๙	บาท
ยอดรวมที่ผู้ใช้ไฟต้องชำระ	๒๒๒,๕๗๒.๐๙	บาท
๔.๒. ค่าใช้จ่ายที่ กฟภ.ลงทุน		
แผนกมิเตอร์	๑,๔๑๓.๐๐	บาท
รวม	๑,๔๑๓.๐๐	บาท

๕. เงื่อนไขและการกำหนดทรัพย์สิน

๕.๑. ค่าใช้จ่ายที่เรียกเก็บจากลูกค้ามีกำหนดยื่นราคา ๑๘๐ วัน นับตั้งแต่วันที่ออกหนังสือแจ้งค่าใช้จ่าย

๕.๒. เมื่อก่อสร้างแล้วเสร็จ ทรัพย์สินในแผนกหม้อแปลงเป็นทรัพย์สินของลูกค้าที่จะต้องดูแลและบำรุงรักษาเองยกเว้นมิเตอร์เป็นทรัพย์สินของการไฟฟ้าส่วนภูมิภาค

๕.๓. ตามอนุมัติ ผจก.กฟส.หาดใหญ่ เลขที่ ต.ทกฟส.หญ.ผกส.๗๒๐/๒๕๖๘ ลว. ๓๐ ก.ค. ๖๘ อนุมัติหลักการ บันทึกค่าใช้จ่ายหน้างาน งานขยายเขตรบบไฟฟ้าสำหรับงานงบบุผู้ใช้ไฟ (งบค) ที่ ๙๐% ของค่าใช้จ่ายหน้างานตามประมาณการ

๕.๔. ทั้งนี้ หากการก่อสร้างระบบไฟฟ้า ดังกล่าวข้างต้น มีความจำเป็นต้องแก้ไข เปลี่ยนแปลง การก่อสร้างฯ หรืออื่นๆ ซึ่งอาจทำให้ค่าใช้จ่ายเพิ่มขึ้น การไฟฟ้าส่วนภูมิภาค จำเป็นต้องเรียกเก็บค่าใช้จ่ายในส่วนที่เพิ่มขึ้นภายหลังอีกต่างหาก ด้วย

จึงเรียนมาเพื่อโปรดพิจารณาอนุมัติ ทั้งนี้ลูกค้าต้องชำระค่าใช้จ่ายตามระเบียบ หรือได้ปฏิบัติ ตามข้อตกลงเรียบร้อยแล้วจึงจะดำเนินการได้

(นายสรายุทธ จุลจินดา)

ผผ.บส.กฟส.หาดใหญ่

...../...../.....

ที่ บส.-[๐๓๘๒]

ผบบ.,ผบส.,ผมต.,ผคพ.,ผบร.,ผกส.หญ.



อนุมัติในหลักการและดำเนินการในส่วนที่เกี่ยวข้อง

(นายโชคชัย ชาญกุล)

ผจก.กฟส.หาดใหญ่



C-69-L-HAYSR.0382

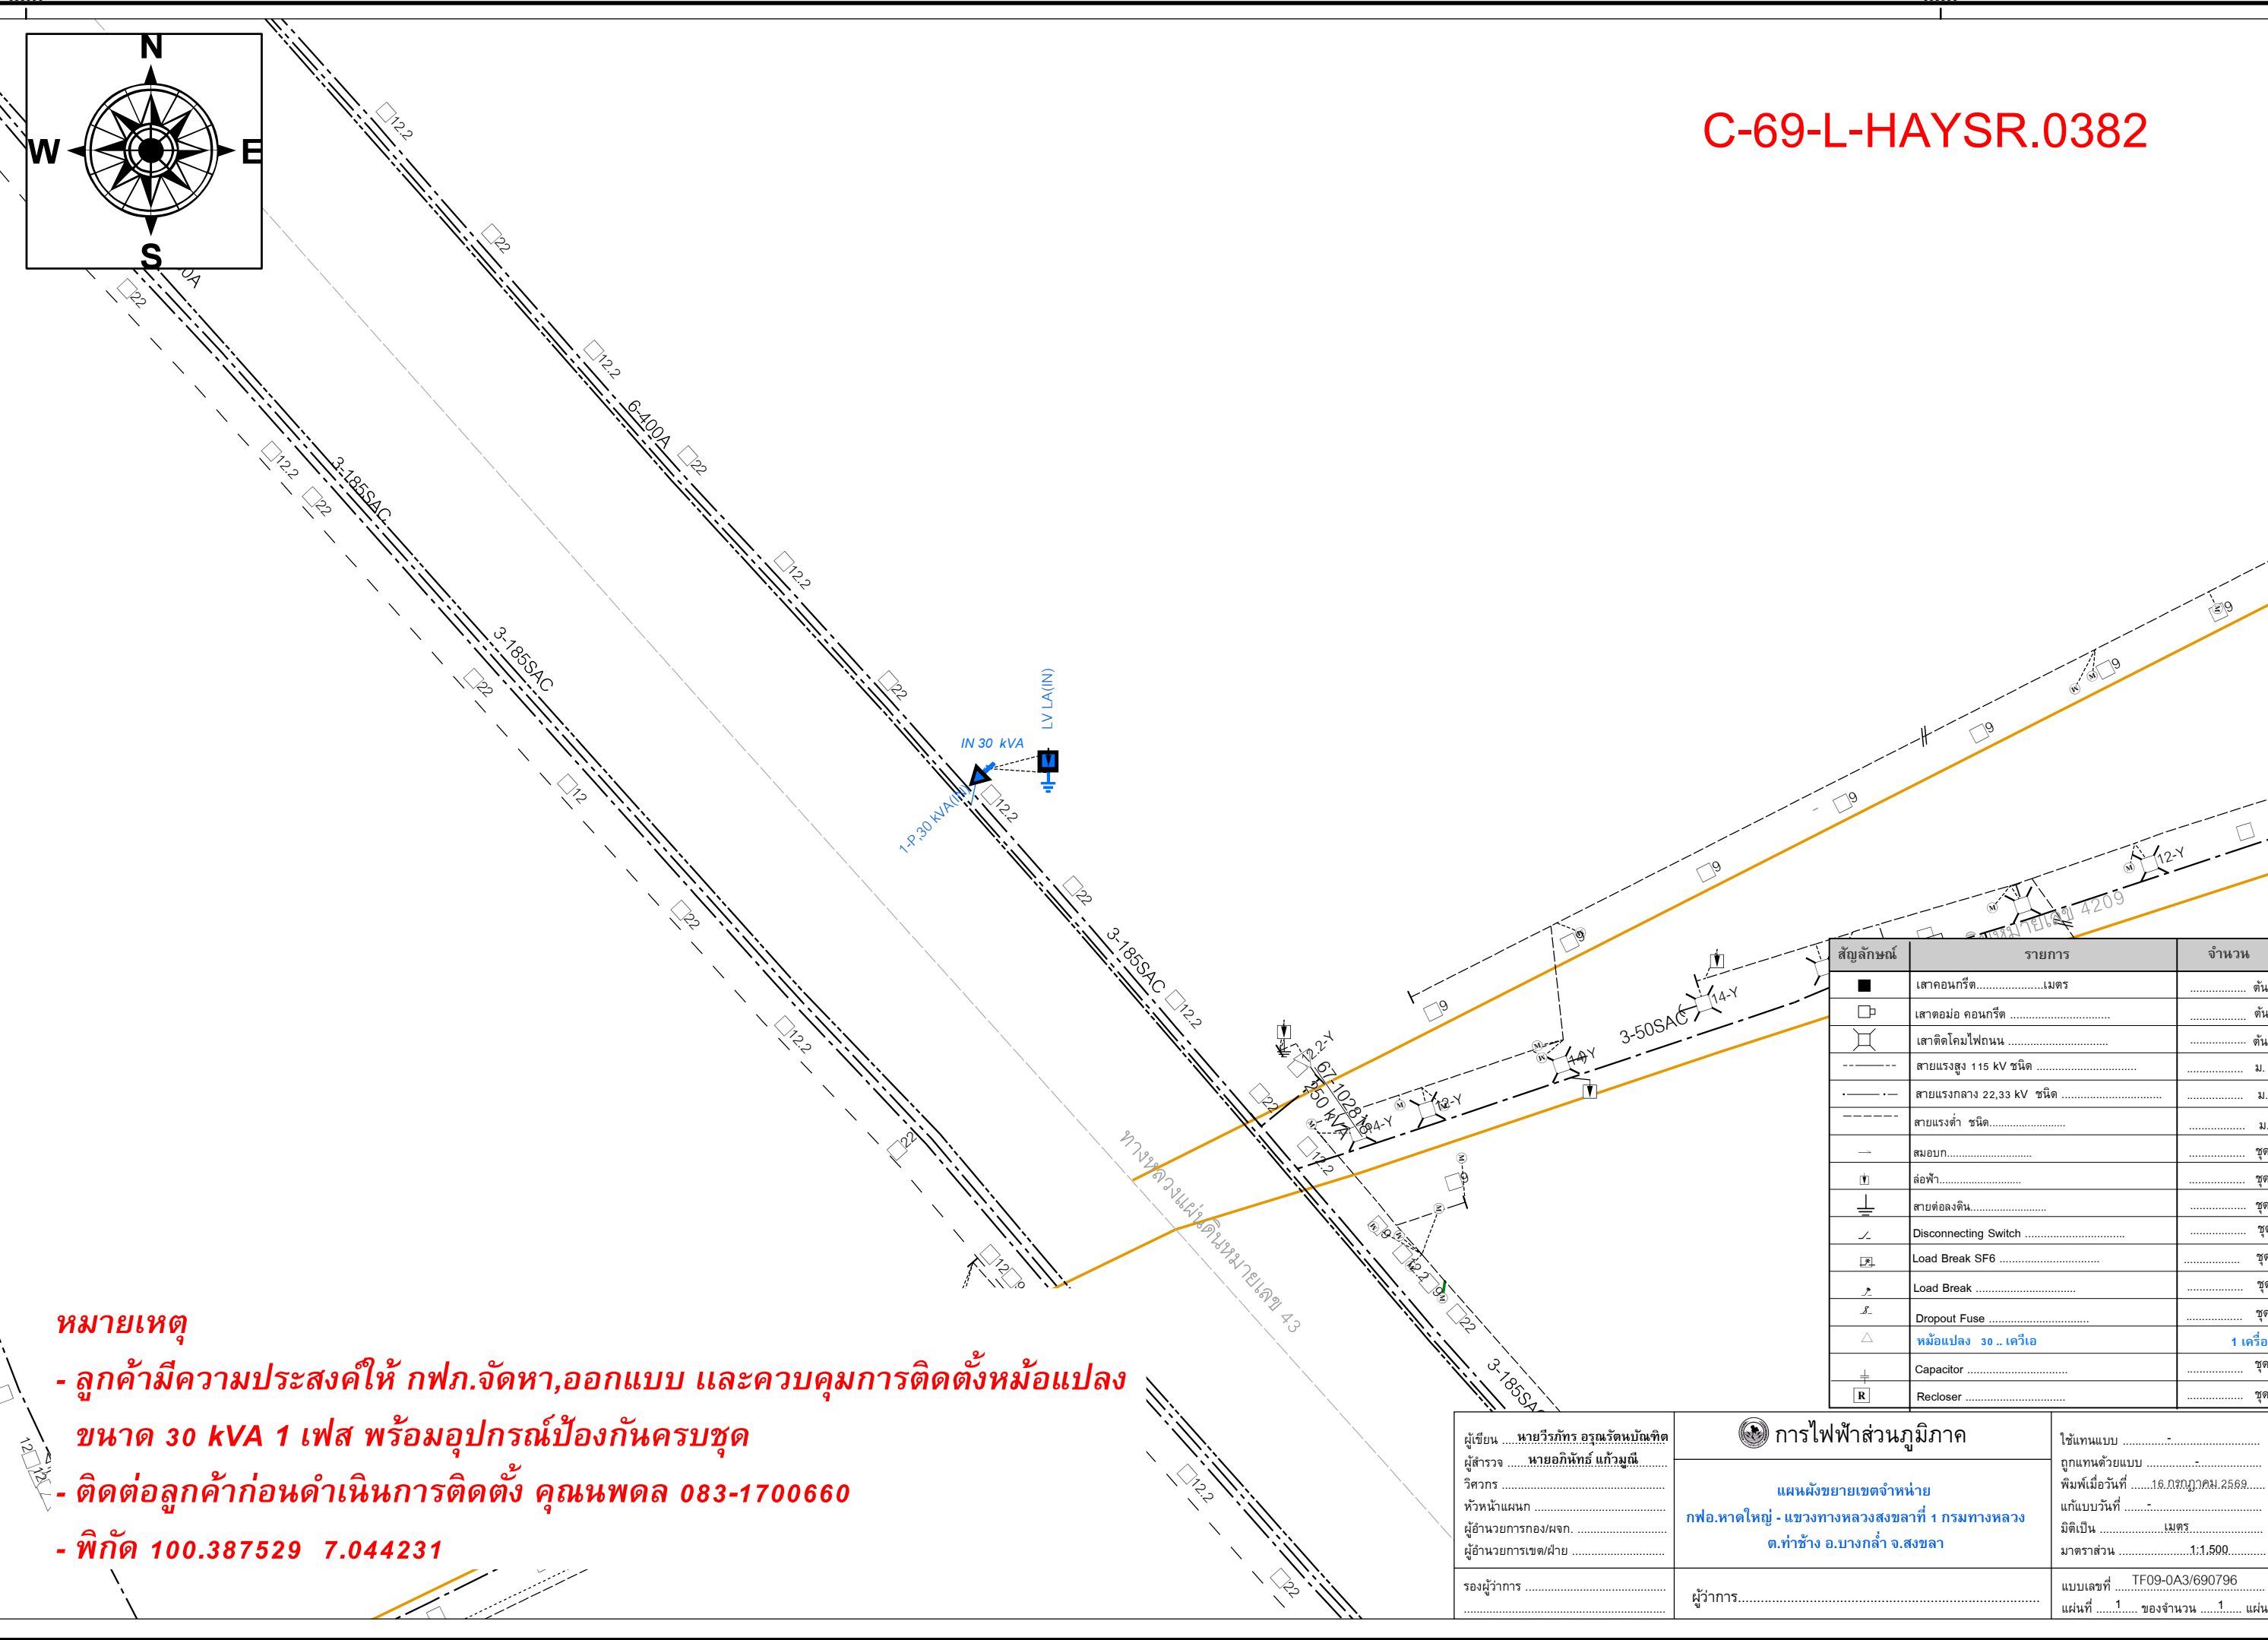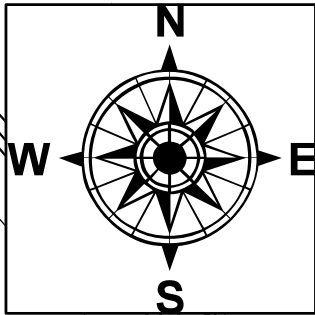

หมายเหตุ

- ลูกค้ำมีความประสงค์ให้ กฟภ.จัดหา,ออกแบบ และควบคุมการติดตั้งหม้อแปลงขนาด 30 kVA 1 เฟส พร้อมอุปกรณ์ป้องกันครบชุด
- ติดต่อลูกค้ำก่อนดำเนินการติดตั้ง คุณนพดล 083-1700660
- พิกัด 100.387529 7.044231

สัญลักษณ์	รายการ	จำนวน
■	เสาคอนกรีต.....เมตร	 ต้น
□	เสาตอม่อ คอนกรีต	 ต้น
⊞	เสาติดโคมไฟถนน	 ต้น
----	สายแรงสูง 115 KV ชนิด	 ม.
----	สายแรงกลาง 22.33 KV ชนิด	 ม.
----	สายแรงต่ำ ชนิด.....	 ม.
—	สมอบก.....	 ชุด
⏏	ส่อฟ้า.....	 ชุด
⏏	สายต่อลงดิน.....	 ชุด
⏏	Disconnecting Switch	 ชุด
⏏	Load Break SF6	 ชุด
⏏	Load Break	 ชุด
⏏	Dropout Fuse	 ชุด
△	หม้อแปลง 30 .. เครื่อ	1 เครื่อง
⏏	Capacitor	 ชุด
R	Recloser	 ชุด

ผู้เขียน นายวิรัชกร อรุณรัตน์บัณฑิต	การไฟฟ้าส่วนภูมิภาค	ใช้แทนแบบ
ผู้สำรวจ นายอภิสิทธิ์ แก้วมณี		ถูกแทนด้วยแบบ
วิศวกร	แผนผังขยายเขตจำหน่าย กฟอ.หาดใหญ่ - แขวงทางหลวงสงขลาที่ 1 กรมทางหลวง ต.ท่าช้าง อ.บางกล่ำ จ.สงขลา	พิมพ์เมื่อวันที่16.07.2569.....
หัวหน้าแผนก		แก้แบบวันที่
ผู้อำนวยการกอง/ผก.	ผู้ว่าการ.....	มิติเป็น เมตร
ผู้อำนวยการเขต/ฝ่าย		มาตราส่วน1:1,500.....
รองผู้ว่าการ	ผู้ว่าการ.....	แบบเลขที่ TF09-0A3/690796
.....		แผ่นที่ 1..... ของจำนวน 1..... แผ่น

สรุปค่าใช้จ่ายในการประมาณการก่อสร้างระบบจำหน่าย

งานที่ เลขที่แบบ TF09-0A3/690796 เขต 3 ภาคใต้
ชื่องาน แขวงทางหลวงสงขลาที่ 1 หน้าศูนย์กระจายสินค้า (จุดที่ 2) บ้านเลขที่ หน้าศูนย์กระจายสินค้า (จุดที่ 2) ตำบลท่าช้าง
อำเภอบางกล่ำ จังหวัดสงขลา 90110

C-69-L-HAYSR.0382

ค่าใช้จ่ายที่ กฟภ.ลงทุน

1. แผนกมิเตอร์	1,413.00	บาท
รวมเงิน	1,413.00	บาท

ค่าใช้จ่ายที่ คิดจากผู้ใช้ไฟ

1. แผนกหม้อแปลงภายใน	150,467.83	บาท
2. อุปกรณ์จับยึดหม้อแปลงป้องกันการโจรกรรม (Nut lock)	3,000.00	บาท
3. แผนกหม้อแปลงภายใน(ชุดกราวด์แรงต่ำทองแดง)	5,708.25	บาท
รวมเงิน	159,176.08	บาท

ค่าธรรมเนียม

1. ค่าสมทบแรงสูง (30 คิวเช100)	3,000.00	บาท
2. ค่าเชื่อมแรงสูง	14,000.00	บาท
3. กำไรขั้นต้น	31,835.22	บาท
รวมเงิน	48,835.22	บาท

รวมเงินค่าใช้จ่ายคิดจากผู้ใช้ไฟ	208,011.30	บาท
---------------------------------	------------	-----

ภาษีมูลค่าเพิ่ม 7 %	14,560.79	บาท
---------------------	-----------	-----

รวมเงินค่าใช้จ่ายคิดจากผู้ใช้ไฟ รวมภาษีมูลค่าเพิ่ม	222,572.09	บาท
--	------------	-----

หมายเหตุ ยังไม่รวมค่าธรรมเนียมต่าง ๆ ขอให้คิดค่าธรรมเนียมตามระเบียบของ กฟภ.ที่กำหนด นอกโปรแกรมประมาณการ ฯ

ผู้สำรวจ	นายอภิสิทธิ์ แก้วมุณี
ผู้ประมาณการ	นายอภิสิทธิ์ แก้วมุณี
ผู้ตรวจสอบ	นายธีรพงศ์ นานั่ง

สรุปค่าใช้จ่ายในการประมาณการก่อสร้างระบบจำหน่าย

งานที่เลขที่แบบTF09-0A3/690796

ชื่องาน

แขวงทางหลวงสงขลาที่ 1 หน้าศูนย์กระจายสินค้า (จุดที่ 2) บ้านเลขที่ หน้าศูนย์กระจายสินค้า (จุดที่ 2) ตำบลท่าช้าง อำเภอบางกล่ำ จังหวัดสงขลา 90110

*** รายละเอียดแสดงการคิดกำไรขั้นต้น (คิดเฉพาะงานที่ก่อสร้างแล้วเสร็จทรัพย์สินเป็นของผู้ใช้ไฟ) ***

แผนงาน	ต้นทุน (บาท)	%กำไรขั้นต้น (%)	กำไรขั้นต้น (บาท)	หมายเหตุ (คำวัสดุอุปกรณ์)	รวม
แผนกหม้อแปลงภายใน	150,467.83	20.00%	30,093.57		180,561.40
อุปกรณ์จับยึดหม้อแปลงป้องกันการโจรกรรม (Nut l	3,000.00	20.00%	600.00		3,600.00
แผนกหม้อแปลงภายใน(ชุดกราวด์แรงต่ำทองแดง)	5,708.25	20.00%	1,141.65		6,849.90
รวม	159,176.08		31,835.22		191,011.30
กำไรขั้นต้น			31,835.22	บาท	31,835.22

ผู้สำรวจนายอภิสิทธิ์ แก้วมุณี

ผู้ประมาณการนายอภิสิทธิ์ แก้วมุณี

ผู้ตรวจสอบนายธีรพงศ์ นานั่ง

Quotation
ใบเสนอราคา

ต้นฉบับ / Original

QT-000004578

ชื่อลูกค้า การไฟฟ้าส่วนภูมิภาคอำเภอหาดใหญ่

Customer Name

เลขที่ผู้เสียภาษี 0-9940-00165-50-1 (สำนักงานใหญ่)

Tax ID

ที่อยู่ หาดใหญ่

Address

วันที่ :

Issue Date

พนักงานขาย : -

Salesman

การชำระเงิน : -

Credit Term

ผู้ติดต่อ :

Contact Name

ชื่อโปรเจกต์ : หม้อแปลง30-160kVA ทองแดง 35

Project Name

เลขที่ No.	รายการ Description	จำนวน Quantity	ราคา/หน่วย Unit Price	ส่วนลด Discount	จำนวนเงิน (THB) Amount
1	แท่งกรวด 5/8 2.4 เมตร	1	380.00	0.00	380.00
2	สาย THW 35	20	190.00	0.00	3,800.00
3	ท่อเหล็ก 3/4	3	60.00	0.00	180.00
4	ข้อโค้งเหล็ก 3/4	1	10.00	0.00	10.00
5	วันตาม CGE-135-5/8	1	190.00	0.00	190.00
6	หางปลา 2 รู 35	1	150.00	0.00	150.00

จำนวน
เงิน
Amount

ห้าพันสามสิบเก้าบาทเจ็ดสิบสตางค์

รวมเป็นเงิน
Subtotal

4,710.00

หักส่วนลดพิเศษ
Special Discount

0.00

ยอดรวมหลังหักส่วนลด
After Discount

4,710.00

จำนวนภาษีมูลค่าเพิ่ม 7 %
Value Added Tax

329.70

จำนวนเงินรวมทั้งสิ้น
Total

5,039.70

หมายเหตุและเงื่อนไข (Terms & Conditions)

เลขบัญชีในการโอน
บิลเอกราช
ชื่อ: หจก.ศูนย์รวมไฟฟ้า
ธนาคารกรุงไทย
เลขที่บัญชี: 017-0-39197-3
บิลเอกราช
ชื่อ: หจก.ศูนย์รวมไฟฟ้า
ธนาคารไทยพาณิชย์
เลขที่บัญชี: 762-214545-8

บิลไม่มีภาษี
ชื่อ: นางสุมาลี แซ่ลิ่ม
ธนาคารไทยพาณิชย์
เลขที่บัญชี: 4096210926

ผู้มอบคำสั่งซื้อ / Customer Signature
วันที่ / Date -----

พนักงานขาย / Sale Person
วันที่ / Date -----

ผู้มีอำนาจลงนาม / Authorized Signature
วันที่ / Date -----

อุปกรณ์ไฟฟ้าทุกชนิดไม่ยืมราคามะคะ เปลี่ยนตามราคาโรงงาน ลูกค้าต้องการสั่งซื้อครบถ้วนเช็คราคาอุปกรณ์ไฟฟ้าอีกครั้งนะคะ ขอบคุณที่ใช้บริการ

หม้อแปลง 30-160 kVA (สายทองแดง 35 ตร.มม.)

ชื่องาน ขว่งทางหลวงสงขลาที่ 1 หน้าศูนย์กระจายสินค้า (จุดที่ 2)			เลขแผนผัง TF09-OA3/690796		
รายการ	จำนวน	หน่วยละ	รวม	ราคา กฟภ.	ค่าแรง
กราวด์รีดหุ้มทองแดง 5/8 x 2.4 ม. 1010220002	1	380.00	380.00	380.00	510.00
สายทองแดงหุ้มฉนวน (THW) ขนาด 35 ตร.มม. 1020080609	20	190.00	3,800.00	3,800.00	-
หางปลาสำหรับเข้าปลายสายทองแดง ขนาด 35 ตร.มม. 1020420101	1	150.00	150.00	150.00	-
ท่อเหล็อง PVC ขนาด 3/4" 1080040001	3	60.00	180.00	180.00	-
ข้อโค้งท่อเหล็อง ขนาด 3/4"	1	10.00	10.00	10.00	-
One Time Mould ชนิด 1 ทาง สำหรับสาย ขนาด 35 ตร.มม. 9090011007	1	190.00	190.00	190.00	90.00
รวม				4,710.00	600.00
รวมค่าวัสดุ+ค่าแรง				5,310.00	
ค่าดำเนินการ 7.5%				398.25	
รวมทั้งสิ้น				5,708.25	

หมายเหตุ

สืบราคาจาก ห้างหุ้นส่วนจำกัด ศูนย์รวมไฟฟ้า 336/1 ถ.ศรีภูวนารถ อ.หาดใหญ่ จ.สงขลา 90110

ตามใบเสนอราคา เลขที่ QT-000004578

ผู้สำรวจ นายอภิสิทธิ์ แก้วมุณี

ผู้ประมาณการ นายอภิสิทธิ์ แก้วมุณี

ผู้ตรวจสอบ นายธีรพงศ์ นาพนัง



การไฟฟ้าส่วนภูมิภาค
บันทึก

จาก
เลขที่
เรื่อง
อ้างถึง

ผู้จัดทำ-ตรวจสอบประมาณการ

ถึง
วันที่
พ.บ.ส.

รายละเอียดประมาณการการไฟฟ้าอำเภอหาดใหญ่ - ชื่องาน แขนงทางหลวงสงขลาที่ 1 หน้าศูนย์กระจาย หมายเลขงาน C-69-L-HAYSR.0382.02.2

เรียน พ.บ.ส. ผ่าน พ.บ.ส.

ตามคำสั่งให้กระผม นายอภิสิทธิ์ แก้วมูณี รหัส 00512977 แผนก ผบส. การไฟฟ้าอำเภอหาดใหญ่ ดำเนินการประมาณการชื่องาน แขนงทางหลวงสงขลาที่ 1 หน้าศูนย์กระจาย สถานที่ก่อสร้าง - ถนน - ตำบล ต.ท่าช้าง อำเภอ อ.บางกล่ำ จังหวัด จ.สงขลา ตามหมายเลขใบสั่งงานด้านล่างนี้ งานดังกล่าวมีปริมาณงานติดตั้งหม้อแปลงใหม่/ติดตั้งเพิ่มเติมจากเดิม(กฟภ.จัดหา)รวม 0.000 KVA หม้อแปลงผู้ใช้ไฟจัดหารวม 0.000 KVA ระยะทางแรงสูงภายใน 0.000 กม. และค่าใช้จ่ายตามประมาณการ ดังนี้

1 C-69-L-HAYSR.0382.02.2 แผนผังเลขที่ TF09-0A3/690796 ศูนย์ต้นทุนที่ร้องขอ L307101000 ศูนย์ต้นทุนที่รับผิดชอบ L307101040 เขตธุรกิจ L071 โรงงาน L070

ที่	แผนก	ปริมาณงาน (วงจร-กม.)	วัสดุนำกลับ มาใช้ใหม่	วัสดุ ใหม่	วัสดุ ใช้งาน	ค่าใช้จ่ายตามประมาณการ(บาท)		ค่าขนส่ง	ค่าเบ็ดเตล็ด	ค่าดำเนินการ	รวม	คชจ.พนักงาน	สัดส่วนต้นทุนการดำเนินงาน(บาท)	
						ค่าจ้างแรงงาน	ค่าควบคุมงาน						กฟภ.ลงทุน(%) 0	ผู้ลงทุน(%) 100
1	TR-C-I	0.000	0.00	115,740.83	2,409.00	9,555.00	2,867.00	5,907.00	6,824.00	7,165.00	150,467.83	25,153.00	0.00	150,467.83
2	TR-C-I	0.000	0.00	0.00	0.00	5,310.00	0.00	0.00	0.00	398.25	5,708.25	5,310.00	0.00	5,708.25
3	TR-C-I	0.000	0.00	0.00	3,000.00	0.00	0.00	0.00	0.00	0.00	3,000.00	0.00	0.00	3,000.00
รวม			0.00	115,740.83	5,409.00	14,865.00	2,867.00	5,907.00	6,824.00	7,563.25	159,176.08	30,463.00		
1.ค่าใช้จ่ายพนักงาน(90.00 %)												27,416.70		
2.ค่าวัสดุนำกลับมาใช้ใหม่												0.00		
3.ค่าวัสดุใหม่												115,740.83		
4.ค่าวัสดุใช้งาน												5,409.00		
5.รวมค่าใช้จ่ายในการก่อสร้างครั้งนี้(1+2+3+4)												148,566.53	0.00	148,566.53
คงเหลือ คชจ.พนักงาน (บาท)												3,046.30		

จึงเรียนมาเพื่อโปรดพิจารณา และแจ้งส่วนเกี่ยวข้องดำเนินการต่อไป

(.....)

(.....)

ตำแหน่ง.....

ตำแหน่ง.....

ผู้จัดทำประมาณการ

ผู้ตรวจสอบประมาณการ

ผู้ใช้ : S3HAYSRL03
โคลเอนท์ : PED-400
โปรแกรม : ZPSF009

การไฟฟ้าส่วนภูมิภาค
ประมาณการพัสดุและค่าใช้จ่าย

วันที่ : 23.07.2026
เวลา : 13:48:46
หน้าที่ : 1

โครงการ C-69-L-HAY - งบประมาณปี69 กฟพ.จตุรรมงาน อ.หาดใหญ่ กฟพ. HAY - การไฟฟ้าอํเภอหาดใหญ่
หมายเลขใบสั่งงาน C-69-L-HAYSR.0382.02.2 - ขวงทางหลวงสงขลาที่ 1 หน้ศูนย์กระจาย / ชื่อผู้ควบคุมงาน
แผนก 2105 TR-C-I แผนกก่อสร้างหรือเปลงภายใน / เลขที่โครงข่าย 008005360471 / เลขที่ใบจอง 0230067473 / วันที่ต้องการพัสดุ -

กลุ่มพัสดุ	คํอธิบายกลุ่มพัสดุ	รหัสพัสดุ	รายการ (ชื่อพัสดุ)	รหัส BoM	จํนวนพัสดุใน	หน่วย	ราคาต่อหน่วย	รวมจํนวนเงิน	วันที่ต้องการพัสดุ	จํนวนรื้อถอน	จํนวนพัสดุนํกลับมาใช้ใหม่
		1-01-020-0010	BRACE,L SHAPE, 50X10 MM., FOR...		1.000	EA	336.00	336.00	23.07.2026	0.000	
		1-02-018-0008	EPR, HIGH-VOLTAGE INSULATING ...		1.000	EA	140.00	140.00	23.07.2026	0.000	
		1-02-033-0006	HOTLINE BAIL-CLAMP,MAIN 70-18...		1.000	EA	743.00	743.00	23.07.2026	0.000	
		1-02-033-0104	HOTLINE CLAMP,MAIN35-185,TAP5...		1.000	EA	603.00	603.00	23.07.2026	0.000	
		1-04-001-0015	ANIMAL BARRIER		1.000	EA	450.00	450.00	23.07.2026	0.000	
		1-04-001-0016	CUTOUT BRACKET		1.000	EA	628.00	628.00	23.07.2026	0.000	
		1-04-002-0013	H.R.C. FUSE, BLADE CONTACT, 1...		1.000	EA	98.30	98.30	23.07.2026	0.000	
		1-04-002-0102	FSD, FULL INSULATED, 1X400A, ...		1.000	EA	2,824.00	2,824.00	23.07.2026	0.000	
		1-05-000-0206	TR., 30KVA,1P,19-0.48/0.24KV,...		1.000	EA	96,670.00	96,670.00	23.07.2026	0.000	
		1-09-025-0039	VOLTAGE TRANSFORMER BUSHING C...		1.000	EA	280.00	280.00	23.07.2026	0.000	
		1-09-025-0040	DROPOUT FUSE CUTOUT COVERS		1.000	EA	670.00	670.00	23.07.2026	0.000	
		1-09-025-0041	LIGHTNING ARRESTER COVERS		1.000	EA	110.00	110.00	23.07.2026	0.000	
		9-09-001-0025	CONCRETE 1/3/5		1.000	EA	2,100.00	2,100.00	23.07.2026	0.000	
		9-09-001-1007	WELDING PONDER, ST. WIRE 50 S...		3.000	EA	103.00	309.00	23.07.2026	0.000	
*								105,961.30			
	1 Concrete Products	1-00-011-0002	CROSSARM 120X120X3,000 MM.		1.000	EA	940.00	940.00	23.07.2026	0.000	
*	1 Concrete Products							940.00			
	2 Accessories for Concrete	1-01-020-0001	BRACE,FLAT,FOR CROSSARM 30X6X...		2.000	EA	64.20	128.40	23.07.2026	0.000	
*	2 Accessories for Concrete							128.40			
	3 Insulator & Accessories	1-01-010-0000	WIRE,ST. SOLID DIA. 4.0 MM.TI...		0.250	KG	61.80	15.45	23.07.2026	0.000	
		1-03-001-0200	INSULATOR,POST, 7.5 KV.,ANSI ...		1.000	EA	2,637.00	2,637.00	23.07.2026	0.000	
		1-03-003-0000	INSULATOR,SPOOL,CLASS 53-2 TI...		2.000	EA	27.00	54.00	23.07.2026	0.000	
*	3 Insulator & Accessories							2,706.45			
	4 Steel wire & Accessories	1-01-010-0004	ST. WIRE, STRANDED 50/7 SQ.MM...		20.000	M	33.60	672.00	23.07.2026	0.000	
		1-01-023-0000	CLAMP,SINGLE U-BOLT,M.8 (WIRE...		4.000	EA	7.92	31.68	23.07.2026	0.000	
*	4 Steel wire & Accessories							703.68			
	5 Conductor & Accessories	1-02-005-0100	CABLE,AERIAL,AL 33 KV. 1X50 S...		5.000	M	119.00	595.00	23.07.2026	0.000	
		1-02-007-0002	CABLE,AL,750 V,50 SQ.MM. TIS...		23.000	M	26.70	614.10	23.07.2026	0.000	
		1-02-018-0001	TAPE,PVC,O/D,0.18X19X10,000 M...		1.000	EA	6.21	6.21	23.07.2026	0.000	
		1-02-020-0002	TIE WIRE,AL 4.0 MM.		1.000	KG	203.00	203.00	23.07.2026	0.000	
		1-02-030-0102	CONN.,PG,DOUBLE BOLT,AL 25-95...		2.000	EA	20.40	40.80	23.07.2026	0.000	
		1-02-042-0102	CABLE LUG,NEMA 2-HOLE,AL 50 S...		12.000	EA	10.70	128.40	23.07.2026	0.000	
		1-02-042-0400	PIN TERMINAL,FOR AL.CONDUCTOR...		1.000	EA	35.20	35.20	23.07.2026	0.000	
*	5 Conductor & Accessories							1,622.71			
	6 Protection Eq. & Accessories	1-04-000-0100	S.A. 30 KV. 5 KA.		1.000	EA	962.00	962.00	23.07.2026	0.000	
		1-04-000-0300	S.A. 250-500 V. 2.5-5.0 KA		1.000	EA	165.00	165.00	23.07.2026	0.000	
		1-04-001-0100	DROPOUT,FUSE, 33 KV. 100 A.		1.000	EA	3,700.00	3,700.00	23.07.2026	0.000	
		1-04-003-0102	FUSE LINK 33 KV. 3 A.EEI-NEMA...		1.000	EA	112.00	112.00	23.07.2026	0.000	
*	6 Protection Eq. & Accessories							4,939.00			
	7 Transformer & Accessories	1-05-010-0003	BRACKET,ST.,FOR TR. SECONDARY...		2.000	EA	53.00	106.00	23.07.2026	0.000	
*	7 Transformer & Accessories							106.00			
	11 Accessories	1-01-011-0100	BOLT,MACHINE M.12X35 MM.		1.000	EA	14.90	14.90	23.07.2026	0.000	
		1-01-011-0200	BOLT,MACHINE M.16X130 MM.		4.000	EA	21.60	86.40	23.07.2026	0.000	

โครงการ C-69-L-HAY - งบผู้ใช้ไฟปี69 กฟฟ.จตุรรมงาน อ.หาดใหญ่ กฟฟ. HAY - การไฟฟ้าอํเภอหาดใหญ่
หมายเลขใบสั่งงาน C-69-L-HAYSR.0382.02.2 - แขวงทางหลวงสงขลาที่ 1 หน้าศูนย์กระจาย / ชื่อผู้ควบคุมงาน
แผนก 2105 TR-C-I แผนกก่อสร้างหรือเปล่งภายใน / เลขที่โครงข่าย 008005360471 / เลขที่ใบจอง 0230067473 / วันที่ต้องการพัสดุ -

กลุ่มพัสดุ	คํอธิบายกลุ่มพัสดุ	รหัสพัสดุ	รายการ (ชื่อพัสดุ)	รหัส BoM	จํนวนพัสดุใหม่	หน่วย	ราคาต่อหน่วย	รวมจํนวนเงิน	วันที่ต้องการพัสดุ	จํนวนรื้อถอน	จํนวนพัสดุนํากลับมาใช้ใหม่
11	Accessories	1-01-011-0203	BOLT,MACHINE M.16X250 MM.		3.000	EA	34.70	104.10	23.07.2026	0.000	
		1-01-011-0204	BOLT,MACHINE M.16X300 MM.		1.000	EA	41.70	41.70	23.07.2026	0.000	
		1-01-011-0205	BOLT,MACHINE M.16X350 MM.		1.000	EA	46.30	46.30	23.07.2026	0.000	
		1-01-011-0206	BOLT,MACHINE M.16X400 MM.		3.000	EA	52.50	157.50	23.07.2026	0.000	
		1-01-018-0100	WASHER,PLAIN,SQUARE, 52X52X4 ...		12.000	EA	4.95	59.40	23.07.2026	0.000	
		1-01-018-0301	WASHER, LOCK, SPRING, SIZE 16 MM..		1.000	EA	3.59	3.59	23.07.2026	0.000	
		1-01-022-0002	GROUND ROD,60X60X5 MM. 2 M.LG..		1.000	EA	460.00	460.00	23.07.2026	0.000	
* 11	Accessories							973.89			
12	Other	1-08-004-0001	CONDUIT,PVC,RIGID, 20X2500 MM..		3.000	EA	22.80	68.40	23.07.2026	0.000	
* 12	Other							68.40			
** แผนก 2105 TR-C-I แผนกก่อสร้างหรือเปล่งภายใน								118,149.83			

ผู้ประมาณการ	นายอภิสิทธิ์ แก้วมณี	1 ค่าพัสดุใหม่	118,149.83	
		2 ค่าแรง	9,555.00	
		3 ค่าควบคุมงาน	2,867.00	
		4 ค่าขนส่ง	5,907.00	
		5 ค่าเบ็ดเตล็ด	6,824.00	
		6 ค่าคํานึงนการ	7,165.00	
		ยอดเงินรวมทั้งสิ้น	150,467.83	0.00

ประมาณการค่าใช้จ่ายการก่อสร้างระบบจำหน่าย (33 kV - แผนกมิเตอร์)

เลขที่แผนผัง	TF09-0A3/690796	เขตการไฟฟ้า	กฟต. 3 (ยะลา)
ชื่องาน	แขวงทางหลวงสงขลาที่ 1 กรมทางหลวง จุดที่ 2		
ชื่อประเภทงาน	MT.มิเตอร์		
1. การลงทุน	กฟภ.		
2. ทรัพย์สิน	กฟภ.		
3. ระยะทางนำกลับมาใช้งาน	ไม่มี		
4. การขนส่ง	แบบปกติ		
5. ค่าแรงอื่นๆ	กรณีที่ 3		
6. ระดับมลภาวะ	ระดับเล็กน้อย		
วันที่คำนวณ	23 กรกฎาคม 2569	ราคามาตรฐานวัสดุงวดที่	3/2569 ณ วันที่ 30 เมษายน 2569

ลำดับ	รหัสวัสดุ	รายละเอียด	ก่อสร้าง	รื้อถอน	นำกลับมาใช้
1	1020320014	H-CONNECTOR,MAIN AL 35-50,TAP CU 6-10	-2.00		
2	1060050019	ELECTRONIC ENERGY METER, 1-PHASE 2-WIRE,DIRECT CONNECT,	1.00		
3	1060100019	SECURITY SEALS. O/D	1.00		
4	41071	LT METER INS. 1-P,220V. ON 12.20 M. CONCRETE POLE 1 UNIT	1.00		

อภินันท์

อภินันท์

ประมาณการค่าใช้จ่ายการก่อสร้างระบบจำหน่าย (33 kV - แผนกมิเตอร์)

เลขที่แผนผัง	TF09-0A3/690796	เขตการไฟฟ้า	กฟต. 3 (ยะลา)
ชื่องาน	แขวงทางหลวงสงขลาที่ 1 กรมทางหลวง จุดที่ 2		
ชื่อประเภทงาน	MT.มิเตอร์		
วันที่คำนวณ	23 กรกฎาคม 2569	งานติดตั้งใหม่ - วัสดุใหม่ (NEW MATERIAL)	

ลำดับ	รหัสวัสดุ	รายละเอียด	จำนวน/หน่วย	ค่าวัสดุ	ค่าแรง
***** Hardware *****					
1	1010110204	BOLT,MACHINE M.16x300 mm.	2.00 ชุด	83.40	0.00
2	1010110205	BOLT,MACHINE M.16x350 mm.	2.00 ชุด	92.60	0.00
3	1010180100	WASHER,PLAIN,SQUARE,LARGE 52x52x4.5 mm.HOLE DIA. 18 MM. TIS.258	8.00 ชิ้น	39.60	0.00
4	1060050019	ELECTRONIC ENERGY METER, 1-PHASE 2-WIRE,DIRECT CONNECT,	1.00 ชิ้น	435.00	324.00
***** Conductor & Accessory *****					
5	1020200000	TAPE,ARMOR,AL 1x10 mm.	0.03 กก.	7.56	0.00
6	1060100019	SECURITY SEALS. O/D	1.00 ชิ้น	3.17	0.00
***** Meter *****					
7	1060100000	CABLE PLATE, SIZE 2X20X20 CM.	2.00 ชิ้น	63.60	0.00
8	1060100001	METER PLATE, SIZE 2X20X60 CM.	1.00 ชิ้น	95.30	0.00
รวมเงิน (ค่าวัสดุ, ค่าแรง) ของแรงงานติดตั้งโดยใช้วัสดุใหม่ (บาท)				820	324
รวมเงิน (ค่าวัสดุ, ค่าแรง) ของ งานติดตั้งใหม่ - วัสดุใหม่ (NEW MATERIAL) (บาท)				820	324
ค่าควบคุมงาน	30.00 %	ของค่าแรง	(324)		97
ค่าขนส่ง	5.00 %	ของค่าวัสดุ	(820)		41
ค่าเบ็ดเตล็ด	5.00 %	ของค่าใช้จ่ายทั้งหมด	(1,282)		64
ค่าดำเนินการ	5.00 %	ของค่าใช้จ่ายรวมทั้งหมด	(1,346)		67
รวมเป็นเงินทั้งสิ้น (ค่าวัสดุ + ค่าแรง + ค่าควบคุมงาน + ค่าขนส่ง + ค่าเบ็ดเตล็ด + ค่าดำเนินการ) ของงานก่อสร้าง (บาท)					1,413

หมายเหตุ 1. ใช้ ราคามาตรฐานวัสดุ การไฟฟ้าส่วนภูมิภาค ประจำปี 3/2569 ณ วันที่ 30 เมษายน 2569
2. จำนวนเงินดังกล่าวเป็นเพียงราคาต้นทุนเท่านั้น กรณีของงานที่ก่อสร้างแล้วเสร็จทรัพย์สินเป็นของผู้ใช้ไฟฟ้า การคิดกำไรให้ดูจากรายงานสรุปราคาค่าใช้จ่ายในการประมาณการฯ และ รายงานแสดงรายละเอียดการคิดกำไรขั้นต้น

ประมาณการค่าใช้จ่ายการก่อสร้างระบบจำหน่าย (33 kV - แผนกหม้อแปลง)

เลขที่แผนผัง	TF09-0A3/690796	เขตการไฟฟ้า	กฟต. 3 (ยะลา)
ชื่องาน	แขวงทางหลวงสงขลาที่ 1 กรมทางหลวง จุดที่ 2		
ชื่อประเภทงาน	TR.แผนกหม้อแปลงภายใน		
1. การลงทุน	ผู้ใช้ไฟ	9. ค่าแรงเสา - กราวด์	กรณีที่ 3
2. ทรัพย์สิน	ผู้ใช้ไฟ	10. งานฐานรากและรั้ว TR	ไม่มี
3. ระยะทางนำกลับมาใช้งาน	ไม่มี		
4. การขนส่ง	แบบปกติ		
5. ค่าแรงอื่นๆ	กรณีที่ 3		
6. ระดับมลภาวะ	ระดับเล็กน้อย		
7. การจัดหาหม้อแปลง	กฟภ. เป็นผู้ดำเนินการ		
8. การเช่าอุปกรณ์หม้อแปลง	ไม่เช่า		
วันที่คำนวณ	23 กรกฎาคม 2569	ราคามาตรฐานพัสดุงวดที่	3/2569 ณ วันที่ 30 เมษายน 2569

ลำดับ	รหัสพัสดุ	รายละเอียด	ก่อสร้าง	รื้อถอน	นำกลับมาใช้
1	1000110000	CROSSARM,PRESTRESSED CONCRETE, 100X100X1,500 MM.	-1.00		
2	1010110100	BOLT,MATCHINE M.12X35 MM.	1.00		
3	1010110206	BOLT,MACHINE M.16x400 mm.	2.00		
4	1010200001	BRACE,FLAT,FOR CROSSARM 30x6x760 mm.	-2.00		
5	1010200010	BRACE,L SHAPE, 50X10 MM., FOR FSD	1.00		
6	1020070002	CABLE,AL,COMPACT STRANDED,PVC-INSULATED,750 V. 75 DEG.C, 50 SQ.MM. TIS.293	5.00		
7	1020180003	ELECTRICAL SPLICING TAPE,FOR H.T.AERIAL CABLE,SIZE 3/4"X30'	-1.00		
8	1020180008	EPR, HIGH-VOLTAGE INSULATING TAPE	1.00		
9	1020330005	HOTLINE BAIL-CLAMP,MAIN 35-70 SQ.MM.	-1.00		
10	1020330006	HOTLINE BAIL-CLAMP,MAIN 70-185 SQ.MM.	1.00		
11	1020420102	CABLE LUG,NEMA HOLE,COMPRESSION TYPE,AL 50 SQ.MM.	4.00		
12	1030010200	INSULATOR,POST, 7.5 KV.,ANSI TR-202	1.00		
13	1040000100	S.A. 30 KV. 5 KA.	1.00		
14	1040000106	S.A., 30 kv.5ka.,WITHOUT BRACKET	-1.00		
15	1040000300	LIGHTNING ARRESTER 250-500 V. 2.5-5.0 kA.	1.00		
16	1040010015	ANIMAL BARRIER	1.00		
17	1040010016	CUTOUT BRACKET	1.00		
18	1040020013	H.R.C. FUSE, BLADE CONTACT, 100 A	1.00		
19	1040020100	L.T. FUSE-SWITCHES 1x400 A. 500 V.	-1.00		
20	1040020102	FSD, FULL INSULATED, 1X400A, 400V	1.00		

ประมาณการค่าใช้จ่ายการก่อสร้างระบบจำหน่าย (33 kV - แผนกหม้อแปลง)

เลขที่แผนผัง	TF09-0A3/690796	เขตการไฟฟ้า	กฟต. 3 (ยะลา)
ชื่องาน	แขวงทางหลวงสงขลาที่ 1 กรมทางหลวง จุดที่ 2		
ชื่อประเภทงาน	TR.แผนกหม้อแปลงภายใน		
1. การลงทุน	ผู้ใช้ไฟ	9. ค่าแรงเสา - กราวด์	กรณีที่ 3
2. ทรัพย์สิน	ผู้ใช้ไฟ	10. งานฐานรากและรั้ว TR	ไม่มี
3. ระยะทางนำกลับมาใช้งาน	ไม่มี		
4. การขนส่ง	แบบปกติ		
5. ค่าแรงอื่นๆ	กรณีที่ 3		
6. ระดับมลภาวะ	ระดับเล็กน้อย		
7. การจัดหาหม้อแปลง	กฟภ. เป็นผู้ดำเนินการ		
8. การเช่าอุปกรณ์หม้อแปลง	ไม่เช่า		
วันที่คำนวณ	23 กรกฎาคม 2569	ราคามาตรฐานวัสดุงวดที่	3/2569 ณ วันที่ 30 เมษายน 2569

ลำดับ	รหัสวัสดุ	รายละเอียด	ก่อสร้าง	รื้อถอน	นำกลับมาใช้
21	1050000206	TR., 30KVA,1P,19-0.48/0.24KV, SC	1.00		
22	1090250039	VOLTAGE TRANSFORMER BUSHING COVERS	1.00		
23	1090250041	LIGHTNING ARRESTER COVERS	1.00		
24	9090010025	CONCRETE 1/3/5	1.00		
25	9090010035	คอมปาวด์ช่วยการสัมผัสทางไฟฟ้า	-1.00		
26	14145	X-ARM-C, INST. WITH 1-LT. SWITCH (1-P, 2-WIRE) (12.20 ,14 M)	1.00		
27	40122	LT WIRING, 50 SQ.MM., 1-P, 2-WIRE, TO METER	1.00		
28	40302	TR.INST., 1-P, 19 KV. ON SINGLE POLE, X-ARM. (12.20 M)(ASSEMBLY NO.3701B)	1.00		

อภินันท์

อภินันท์

ประมาณการค่าใช้จ่ายการก่อสร้างระบบจำหน่าย (33 kV - แผนกหม้อแปลง)

เลขที่แผนผัง	TF09-0A3/690796	เขตการไฟฟ้า	กฟต. 3 (ยะลา)
ชื่องาน	แขวงทางหลวงสงขลาที่ 1 กรมทางหลวง จุดที่ 2		
ชื่อประเภทงาน	TR.แผนกหม้อแปลงภายใน		
วันที่คำนวณ	23 กรกฎาคม 2569	งานติดตั้งใหม่ - วัสดุใหม่ (NEW MATERIAL)	

ลำดับ	รหัสวัสดุ	รายละเอียด	จำนวน/หน่วย	ค่าวัสดุ	ค่าแรง
***** Pole & Stub *****					
1	1000110002	CROSSARM,PRESTRESSED CONCRETE,SPUN,H.T. 120X120X3,000 MM.	1.00 ชิ้น	940.00	248.00
2	9090010025	CONCRETE 1/3/5	1.00 ลบ.ม.	2,100.00	3,225.00
***** Guying *****					
3	1010100000	WIRE,STEEL SOLID DIA. 4.0 mm.TIS.71	0.25 กก.	15.45	0.00
4	1010100004	WIRE,STEEL STRANDED 50/7 sq.mm.TIS.404	20.00 ม.	672.00	0.00
5	1010220002	ROD,GROUND,60x60x5 mm. 2 m.LONG	1.00 ชุด	460.00	660.00
6	1010230000	CLAMP,SINGLE U-BOLT,M.8 (WIRE ROPE CLIP)	4.00 ชุด	31.68	0.00
7	1080040001	CONDUIT,PVC,RIGID,DIA. 20x2500 mm.TIS.216	3.00 ชิ้น	68.40	0.00
8	9090011007	WELDING POWDER, ST. WIRE 50 SQ.MM. TO GD	3.00 ชิ้น	309.00	275.40
***** Hardware *****					
9	1010110100	BOLT,MACHINE M.12X35 MM.	1.00 ชุด	14.90	0.00
10	1010110200	BOLT,MACHINE M.16x130 mm.	4.00 ชุด	86.40	0.00
11	1010110203	BOLT,MACHINE M.16x250 mm.	3.00 ชุด	104.10	0.00
12	1010110204	BOLT,MACHINE M.16x300 mm.	1.00 ชุด	41.70	0.00
13	1010110205	BOLT,MACHINE M.16x350 mm.	1.00 ชุด	46.30	0.00
14	1010110206	BOLT,MACHINE M.16x400 mm.	3.00 ชุด	157.50	0.00
15	1010180100	WASHER,PLAIN,SQUARE,LARGE 52x52x4.5 mm.HOLE DIA. 18 MM. TIS.258	12.00 ชิ้น	59.40	0.00
16	1010180301	WASHER,LOCK,SPRING,SIZE 16 mm.,GENERAL PURPOSE,TIS.259	1.00 ชิ้น	3.59	0.00
17	1010200001	BRACE,FLAT,FOR CROSSARM 30x6x760 mm.	2.00 ชิ้น	128.40	113.00
18	1010200010	BRACE,L SHAPE, 50X10 MM., FOR FSD	1.00 ชิ้น	336.00	146.00
19	1040020102	FSD, FULL INSULATED, 1X400A, 400V	1.00 ชิ้น	2,824.00	146.00
***** Conductor & Accessory *****					
20	1020050100	CABLE,AERIAL,AL 33 kV. 1x50 sq.mm.	5.00 ม.	595.00	0.00
21	1020070002	CABLE,AL,COMPACT STRANDED,PVC-INSULATED,750 V. 75 DEG.C, 50 SQ.MM. TIS.293	23.00 ม.	614.10	0.00
22	1020180001	TAPE,ELECTRICAL,PVC.PLASTIC,OUTDOOR TYPE,ROLL SIZE 0.18X19X10,000 MM. TIS.386	1.00 ม้วน	6.21	0.00
23	1020200002	TIE WIRE,AL 4 mm.	1.00 กก.	203.00	0.00

ประมาณการค่าใช้จ่ายการก่อสร้างระบบจำหน่าย (33 kV - แผนกหม้อแปลง)

ลำดับ	รหัสพัสดุ	รายละเอียด	จำนวน/หน่วย	ค่าวัสดุ	ค่าแรง
24	1020300102	CONNECTOR,PARALLEL GROOVE,DOUBLE BOLT,AL,AL-ALLOY AND ACSR 25-95 SQ.MM.	2.00 ชิ้น	40.80	0.00
25	1020330006	HOTLINE BAIL-CLAMP,MAIN 70-185 SQ.MM.	1.00 ชิ้น	743.00	0.00
26	1020330104	HOTLINE CLAMP,MAIN35-185,TAP50-185SQ.MM.	1.00 ชิ้น	603.00	0.00
27	1020420102	CABLE LUG,NEMA HOLE,COMPRESSION TYPE,AL 50 SQ.MM.	12.00 ชิ้น	128.40	0.00
28	1020420400	PIN TERMINAL,FOR AL 50 SQ.MM.	1.00 ชิ้น	35.20	0.00
***** Insulator *****					
29	1020180008	EPR, HIGH-VOLTAGE INSULATING TAPE	1.00 ชิ้น	140.00	0.00
30	1030010200	INSULATOR,POST, 7.5 KV.,ANSI TR-202	1.00 ชิ้น	2,637.00	146.00
31	1030030000	INSULATOR,SPOOL,TYPE B (CLASS 53-2)TIS.227	2.00 ชิ้น	54.00	0.00
***** Transformer *****					
32	1040000100	S.A. 30 KV. 5 KA.	1.00 ชุด	962.00	146.00
33	1040000300	LIGHTNING ARRESTER 250-500 V. 2.5-5.0 kA.	1.00 ชุด	165.00	135.00
34	1040010015	ANIMAL BARRIER	1.00 ชิ้น	450.00	70.00
35	1040010016	CUTOOUT BRACKET	1.00 ชิ้น	628.00	76.00
36	1040010100	CUT-OUT,FUSE,OPEN TYPE,SINGLE ISULATOR,DROPOUT 33 KV. 100 A.	1.00 ชุด	3,700.00	265.00
37	1040020013	H.R.C. FUSE, BLADE CONTACT, 100 A	1.00 ชิ้น	98.30	0.00
38	1040030102	FUSE LINK 33 kv. 3 A.EEI-NEMA TYPE K OR HIGH SURGE TYPE	1.00 ชิ้น	112.00	0.00
39	1050000206	TR., 30KVA,1P,19-0.48/0.24KV, SC	1.00 ชิ้น	96,670.00	3,704.50
40	1050100003	BRACKET,STEEL,FOR TRANSFORMER SECONDARY LEAD	2.00 ชุด	106.00	0.00
41	1090250039	VOLTAGE TRANSFORMER BUSHING COVERS	1.00 ชิ้น	280.00	43.00
42	1090250040	DROPOUT FUSE CUTOOUT COVERS	1.00 ชิ้น	670.00	113.00
43	1090250041	LIGHTNING ARRESTER COVERS	1.00 ชิ้น	110.00	43.00
รวมเงิน (ค่าวัสดุ, ค่าแรง) ของแรงงานติดตั้งโดยใช้วัสดุใหม่ (บาท)				118,150	9,555
รวมเงิน (ค่าวัสดุ, ค่าแรง) ของ งานติดตั้งใหม่ - วัสดุใหม่ (NEW MATERIAL) (บาท)				118,150	9,555
ค่าควบคุมงาน	30.00 %	ของค่าแรง	(	9,555)	2,867
ค่าขนส่ง	5.00 %	ของค่าวัสดุ	(	118,150)	5,907
ค่าเบ็ดเตล็ด	5.00 %	ของค่าใช้จ่ายทั้งหมด	(	136,479)	6,824
ค่าดำเนินการ	5.00 %	ของค่าใช้จ่ายรวมทั้งหมด	(	143,303)	7,165
รวมเป็นเงินทั้งสิ้น (ค่าวัสดุ + ค่าแรง + ค่าควบคุมงาน + ค่าขนส่ง + ค่าเบ็ดเตล็ด + ค่าดำเนินการ) ของงานก่อสร้าง (บาท)					150,468

หมายเหตุ 1. ใช้ ราคามาตรฐานพัสดุ การไฟฟ้าส่วนภูมิภาค ประจำปีที่ 3/2569 ณ วันที่ 30 เมษายน 2569
 2. จำนวนเงินดังกล่าวเป็นเพียงราคาต้นทุนเท่านั้น กรณีของงานที่ก่อสร้างแล้วเสร็จทรัพย์สินเป็นของผู้ใช้ไฟฟ้า การคิดกำไรให้ดูจากรายงานสรุปราคาค่าใช้จ่ายในการประมาณการฯ และ รายงานแสดงรายละเอียดการคิดกำไรขั้นต้น

อธิบดี

อธิบดี

ผู้สำรวจ นาย อภิสิทธิ์ แก้วมุณี

ผู้ประมาณการ นาย อภิสิทธิ์ แก้วมุณี

ผู้ตรวจสอบ นาย อธิพงศ์ นานนท์

ประมาณการค่าใช้จ่ายการก่อสร้างระบบจำหน่าย

งานที่ TF09-0A3/690796 เขตการไฟฟ้า กฟต. 3 (ยะลา)
 ชื่องาน ขบวนการหลวงสงขลาที่ 1 กรมทางหลวง จุดที่ 2
 ที่อยู่
 เบอร์โทรศัพท์

ค่าใช้จ่ายที่การไฟฟ้าส่วนภูมิภาคลงทุน

1	มิเตอร์ - MT.มิเตอร์	1,413	บาท
	รวมเงิน	1,413	บาท

ค่าใช้จ่ายที่คิดจากผู้ใช้ไฟฟ้า

ระบบจำหน่ายภายใน (02.2)

1	หม้อแปลงภายใน - TR.แผนกหม้อแปลงภายใน	150,468	บาท
	รวมเงิน	150,468	บาท

กำไร (คิดเฉพาะทรัพย์สินผู้ใช้ไฟฟ้า - 02.2)

กำไรขั้นต้น	30,093	บาท
% ลดกำไร	0	%
จำนวนเงินที่ลดราคา	0	บาท
กำไรสุทธิ	30,093	บาท

อภินันท์

อภินันท์



การไฟฟ้าส่วนภูมิภาค
PROVINCIAL ELECTRICITY AUTHORITY

การไฟฟ้าส่วนภูมิภาค

แบบฟอร์มขออนุมัติค่าใช้จ่ายหน้างาน

เรียน ผจก. กฟส.หาดใหญ่

ตามที่ กฟส.หาดใหญ่ ได้มอบหมายให้ ผบส.กฟส.หาดใหญ่ ดำเนินการก่อสร้าง
แนวทางหลวงสงขลาที่ 1 กรมทางหลวง จุดที่ 2

-
ในชั้นนี้เห็นควรอนุมัติค่าใช้จ่ายหน้างานในการก่อสร้าง/รื้อถอน ดังรายการต่อไปนี้

หมายเลขผัง : TF09-0A3/690796

มิเตอร์ - MT.มิเตอร์

รายการ	ประมาณการ (บาท)	ขออนุมัติ (เปอร์เซ็นต์)	อนุมัติ (บาท)	คงเหลือ (บาท)
ค่าแรง	324	90	292	32
ค่าควบคุมงาน	97	90	87	10
ค่าขนส่ง	41	90	37	4
ค่าเบ็ดเตล็ด	64	90	58	6
รวม	526		473	53

หม้อแปลงภายใน - TR.แผนกหม้อแปลงภายใน

รายการ	ประมาณการ (บาท)	ขออนุมัติ (เปอร์เซ็นต์)	อนุมัติ (บาท)	คงเหลือ (บาท)
ค่าแรง	9,555	90	8,600	956
ค่าควบคุมงาน	2,867	90	2,580	287
ค่าขนส่ง	5,907	90	5,316	591
ค่าเบ็ดเตล็ด	6,824	90	6,142	682
รวม	25,153		22,638	2,515

จึงเรียนมาเพื่อโปรดพิจารณาอนุมัติค่าใช้จ่าย (ค่าแรง + ค่าควบคุมงาน + ค่าขนส่ง + ค่าเบ็ดเตล็ด) รวมเป็นเงินทั้งสิ้น
23,111.10 (สองหมื่นสามพันหนึ่งร้อยสิบเอ็ดบาทสิบสตางค์)

โดยให้ ผจก. กฟส.หาดใหญ่ เป็นผู้เบิกและสั่งจ่ายจากเงินรายได้ของ กฟส.หาดใหญ่ ดำเนินการก่อสร้าง
ทั้งนี้หากมีค่าใช้จ่ายในส่วนของผู้ใช้ไฟ ผู้ใช้ไฟต้องชำระค่าใช้จ่ายตามระเบียบหรือได้ปฏิบัติตามข้อตกลงเรียบร้อยแล้วจึงดำเนินการได้

อนุมัติตามเสนอ

ลงชื่อ

ผู้ขออนุมัติ

(นาย สราวุธ จุลจินดา)

ลงชื่อ

ผู้อนุมัติ

ตำแหน่ง

ผบ.บส.กฟส.หญ.

(นาย โชคชัย ชาญกุล)

ตำแหน่ง

ผจก.กฟส.หญ.



การไฟฟ้าส่วนภูมิภาค

PROVINCIAL ELECTRICITY AUTHORITY

ที่ มท ๕๓๐๗.๗๔/กฟส.หญ.(บส).

การไฟฟ้าส่วนภูมิภาคสาขาหาดใหญ่

๑๕๑๘ ถนนเพชรเกษม ตำบลหาดใหญ่

อำเภอหาดใหญ่ จังหวัดสงขลา ๙๐๑๑๐

กรกฎาคม ๒๕๖๙

เรื่อง แจ้งค่าใช้จ่ายในการขยายเขตติดตั้งหม้อแปลงไฟฟ้า

เรียน ผู้อำนวยการแขวงทางหลวงสงขลาที่ ๑

อ้างถึง คำร้องขยายเขตระบบจำหน่ายไฟฟ้า เลขที่ LHAY๖๙๐๐๒๕๐๗ ลงวันที่ ๑๔ ก.ค. ๖๙

ตามหนังสือที่ได้แจ้งความประสงค์ขอให้ การไฟฟ้าส่วนภูมิภาคสาขาหาดใหญ่ ดำเนินการขยายเขตระบบไฟฟ้าให้กับ แขวงทางหลวงสงขลาที่ ๑ จุดที่ ๒ บริเวณ ทางหลวงหมายเลข ๔ ตอนควบคุม ๑๔๐๑ ตอนพรุพอ-เนินพิชัย ระหว่าง กม.๑๒๔๔+๒๕๐-กม.๑๒๔๕+๑๐๐ ตำบลท่าช้าง อำเภอบางกล่ำ จังหวัดสงขลา ตามรายละเอียดแนบมาเรียบร้อยแล้ว นั้น

การไฟฟ้าส่วนภูมิภาคสาขาหาดใหญ่ได้ดำเนินการสำรวจและประมาณการ ค่าใช้จ่ายในการขยายเขต โดยมีรายละเอียดพอสรุปได้ ดังนี้

๑. การดำเนินการ

๑.๑ แผนกหม้อแปลงภายใน

- ติดตั้งหม้อแปลง ขนาด ๓๐ เควีเอ ระบบ ๑ เฟส ๑๙,๐๐๐-๔๘๐/๒๔๐ โวลท์ จำนวน ๑ เครื่อง พร้อมอุปกรณ์ ป้องกันสัต์ว TR ๒๐๒ ครอบชุด (แบบแขวน)
- โดยการไฟฟ้าดำเนินการออกแบบและก่อสร้างเอง

๑.๒. แผนกมิเตอร์

- ติดตั้งมิเตอร์แรงต่ำ ขนาด ๕(๑๐๐) แอมป์ ระบบ ๑ เฟส จำนวน ๑ ชุด
- โดยการไฟฟ้าดำเนินการก่อสร้างเอง

๒. ค่าใช้จ่ายในการดำเนินการ

๒.๑ ค่าใช้จ่ายในการดำเนินการ ตามข้อ ๑.๑-๑.๒	เป็นเงิน	๒๐๕,๐๑๑.๓๐	บาท
๒.๒ ค่าสมทบการก่อสร้าง เควีเอ ละ ๑๐๐ บาท	เป็นเงิน	๓,๐๐๐.๐๐	บาท
รวมค่าใช้จ่าย ข้อ ๒.๑-๒.๒	เป็นเงิน	๒๐๘,๐๑๑.๓๐	บาท
ภาษีมูลค่าเพิ่ม	เป็นเงิน	๑๔,๕๖๐.๗๙	บาท
รวมค่าใช้จ่ายทั้งสิ้น	เป็นเงิน	๒๒๒,๕๗๒.๐๙	บาท

(สองแสนสองหมื่นสองพันห้าร้อยเจ็ดสิบสองบาทเก้าสตางค์)

การไฟฟ้าส่วนภูมิภาค

กำหนดยื่นราคา ภายในระยะเวลา ๑๘๐ วัน นับจากวันที่แจ้งค่าใช้จ่ายฉบับนี้ให้ท่านทราบ เมื่อก่อสร้างแล้วเสร็จ ทรัพย์สินแผนกหม้อแปลง เป็นของท่าน ซึ่งจะต้องดูแลบำรุงรักษาเอง (ยกเว้นเครื่องวัดพลังงานไฟฟ้า และอุปกรณ์ประกอบ)

ทั้งนี้หากการก่อสร้างระบบไฟฟ้า ดังกล่าวข้างต้น มีความจำเป็นต้องแก้ไขเปลี่ยนแปลงการก่อสร้างฯ หรืออื่นๆ ซึ่งอาจทำให้ค่าใช้จ่ายเพิ่มขึ้น การไฟฟ้าส่วนภูมิภาค จำเป็นต้องเรียกเก็บค่าใช้จ่ายในส่วนที่เพิ่มขึ้นภายหลังอีกต่างหากด้วย

การไฟฟ้าส่วนภูมิภาค ขอเรียกเก็บค่าใช้จ่ายในการสำรวจ ออกแบบ จัดทำแผนผัง ประมาณการ เป็นจำนวนเงิน ๕,๓๕๐.- บาท (รวมภาษีมูลค่าเพิ่ม) แต่หากยืนยันให้การไฟฟ้าส่วนภูมิภาค ดำเนินการก่อสร้างระบบไฟฟ้าภายในบริเวณผู้ใช้ไฟ ซึ่งชำระเงินค่าก่อสร้างภายในกำหนดยื่นราคา การไฟฟ้าส่วนภูมิภาค จะยกเว้นไม่เรียกเก็บค่าสำรวจ ออกแบบฯ จำนวนดังกล่าว

อนึ่ง ในการชำระเงินให้กับการไฟฟ้าส่วนภูมิภาค ตามข้อ ๒.๑-๒.๒ ให้ชำระด้วยเช็ครับรองธนาคาร (แคชเชียร์เช็ค), ดราฟท์หรือเงินสดเท่านั้น และโปรดแนบสำเนาแบบแสดงรายการจดทะเบียนภาษีมูลค่าเพิ่ม (ภ.พ.๒๐) มามอบให้การไฟฟ้าส่วนภูมิภาค ด้วย

จึงเรียนมาเพื่อโปรดทราบ หากมีข้อสงสัยประการใด สอบถามรายละเอียดได้ ณ สำนักงานการไฟฟ้าส่วนภูมิภาคสาขาหาดใหญ่ ถนนเพชรเกษม ได้ทุกวันในเวลาเปิดทำการ

ขอแสดงความนับถือ

(นายโชคชัย ชาญกุล)

ผู้จัดการ การไฟฟ้าส่วนภูมิภาคสาขาหาดใหญ่

แผนกบริการและลูกค้าสัมพันธ์

โทรศัพท์ ๐๙๔-๘๐๖๑๒๔



แจ้งหลักฐานการชำระเงิน ฯ

งาน แนวทางหลวงจุดที่ ๒

ผู้ร่าง...../.....

ผู้พิมพ์...../.....

ผู้ตรวจสอบ...../.....

วศก...../.....

นผ...../.....

รกก...../.....